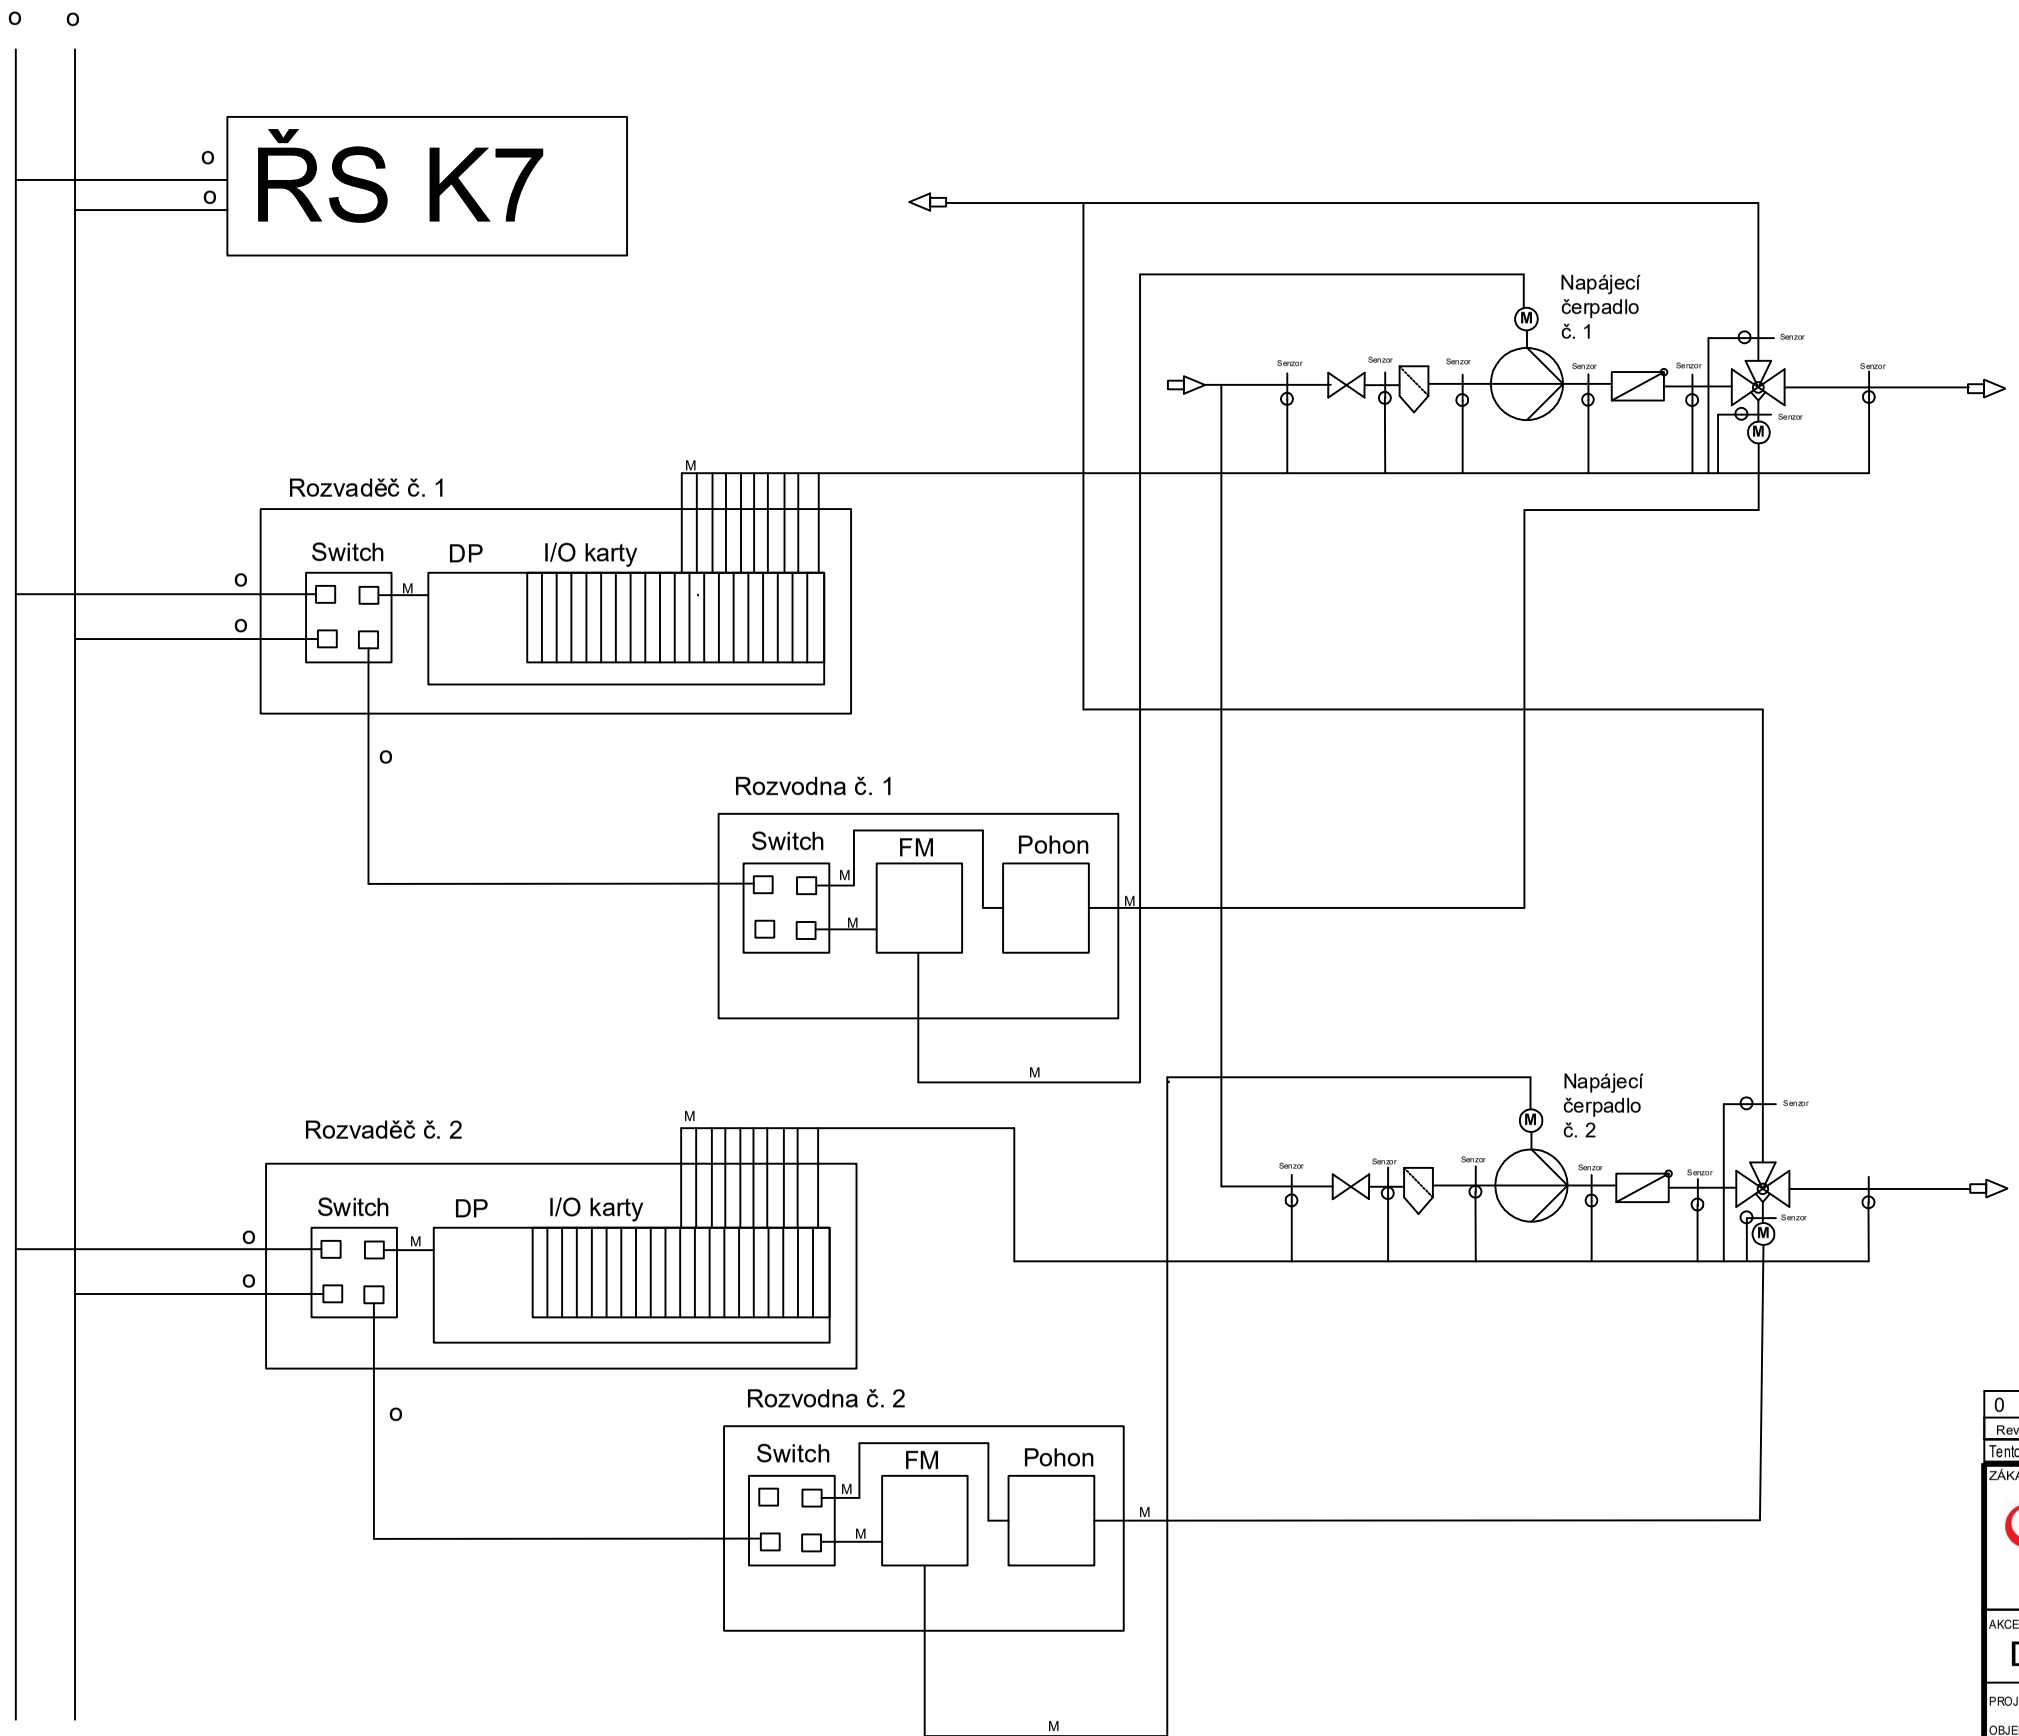



| | | | | | | | | | |
|---|---|---|---|---|---|---|---|---|---|
| 0 | 18.08.2025 | Pracovní revize | 1 | Bláha | | Kasl | | Beran | |
| Rev. | Datum | Popis | Poř.: | Kreslil | Podpis | Kontroloval | Podpis | Schválil | Podpis |

Tento výkres je majetkem projektanta, jeho kopírování, distribuce (zcela nebo částí) je zakázána, pokud to není výslovně povoleno, chráněno pode ISO 16016.

ZÁKAZNÍK:
VEOLIA ENERGIE ČR, a.s.
28. října 3337/7
MORAVSKÁ OSTRAVA,
702 00 OSTRAVA
www.teploprokarvinou.cz

ZHOTOVITEL PROJEKTOVÉ DOKUMENTACE:
TAURES, a.s.
Opletalova 1015/55
110 00 Praha 1
+420 221 594 320
taures@taures.cz
www.taures.cz

AKCE:
Dekarbonizace Teplárny Karviná

SUBDODAVATEL PROJEKTOVÉ DOKUMENTACE:
ALSTACON, s.r.o.
Na dolinách 1272/41 Nusle
140 00 Praha 4
+420 724 590 036
m.mudry@alstacon.com
www.alstacon.com

PROJEKT: TEPLÁRENSKÝ ZDROJ 1 (TG8, K15, chladič horkovodu, akumulace tepla)
OBJEKT: PS 03.06 – MaR, ASŘ, slaboproud

ČÁST DOKUMENTACE:
ZDROJ 1

ZAKÁZKA ČÍSLO: 25A02
POČET A4: ...
MĚŘÍTKO:
STUPEŇ DOKUMENTACE: Technická dokumentace provedení záměru
POŘ. Č.: D2.6.b.1

NÁZEV:
Blokové schéma napájecí čerpadla K7

ČÍSLO VÝKRESU: 25A02-C00R101
REV.: 0